


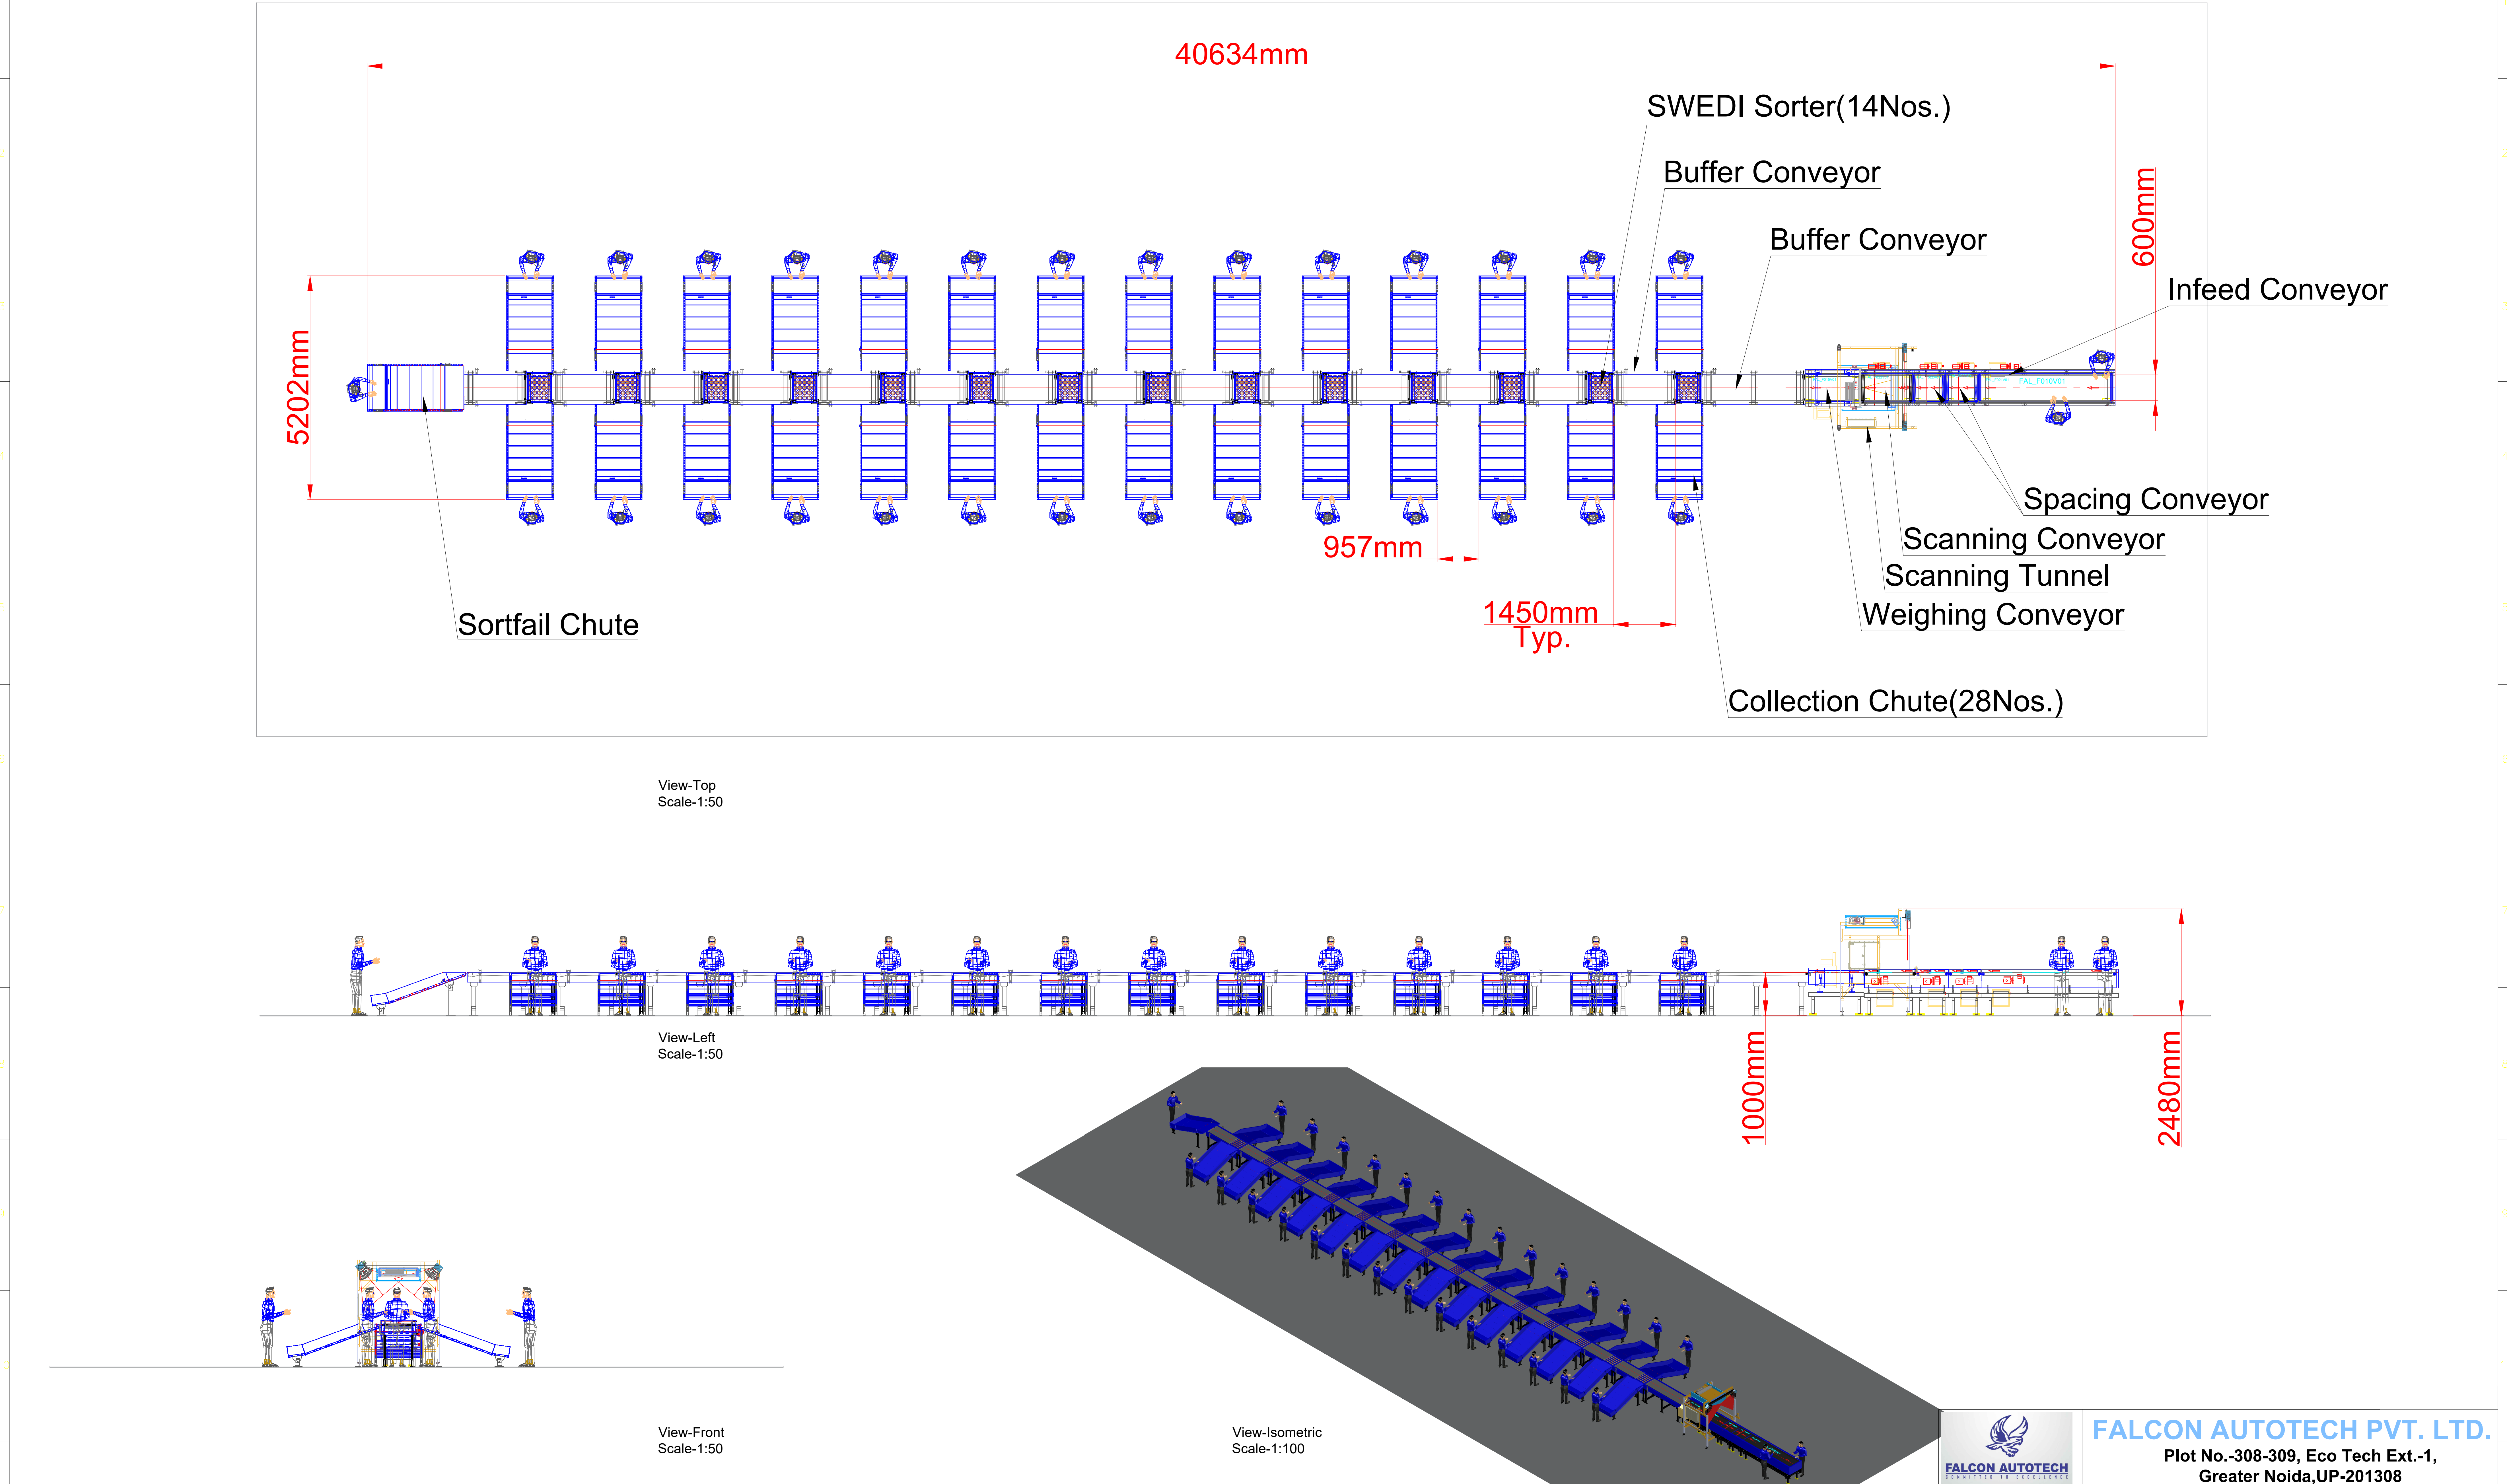

NOTE:- 1- THIS DRAWING IS NOT IN SCALE. 2- 699 MEANING IS THE COMMON CODE FOR PROCESS FLOW DIAGRAM FOR ALL CLIENT. 3- FA/CU MEANING IS FALCON SCOPE / CUSTOMER SCOPE. 4- ALL EQUIPMENT SHAPE/OUTLINE ARE PROJECTIVE NOT IN ACTUAL SCALE.	
---	--	--	